


SCALE 3/16" = 1' - 0"

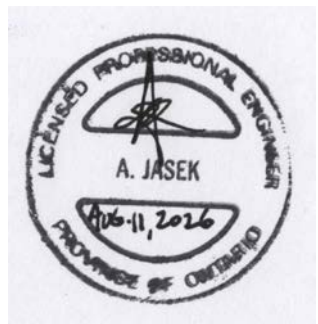

38 Twin Sister Lakes Road
Marmora, Ontario
K0K 2M0
Tel 613-472-2308

ONTARIO ASSOCIATION
OF
ARCHITECTS
Marilyn Ypes
MARILYN A. YPES
LICENCE
3289





LOCATION :
1766 QUEEN'S LINE ROAD
TOWNSHIP OF MINDEN
HILLS

CHECKED

MY

WORKING NO.	
-------------	--

2b

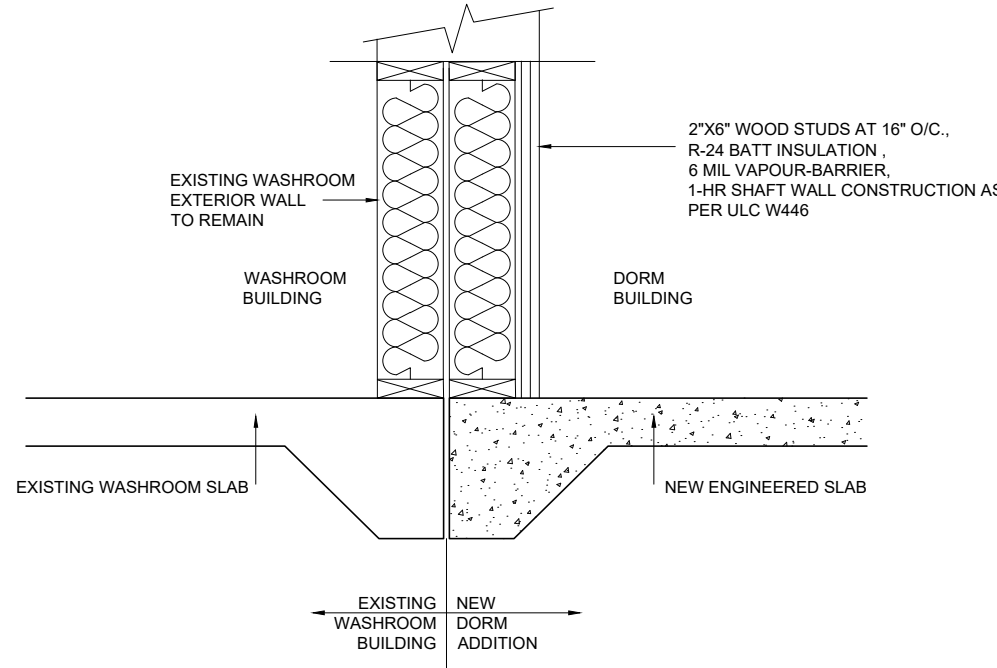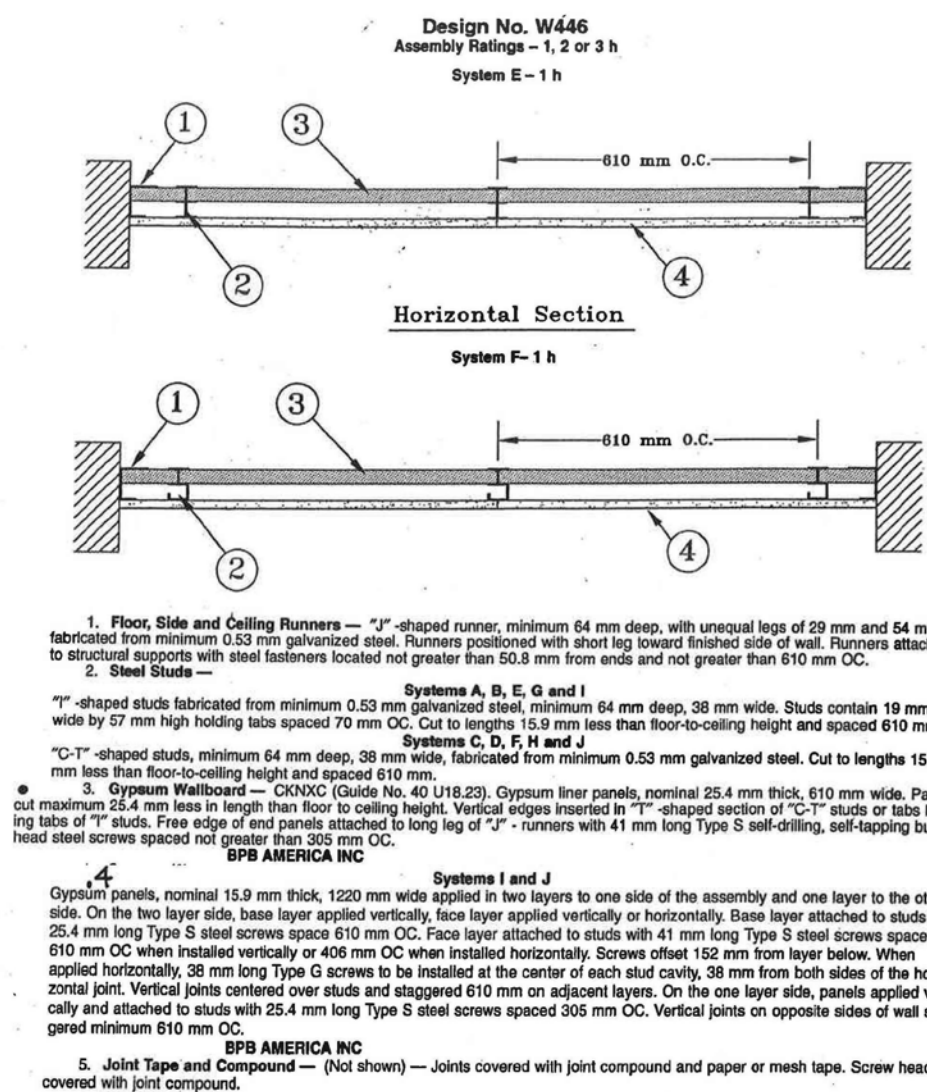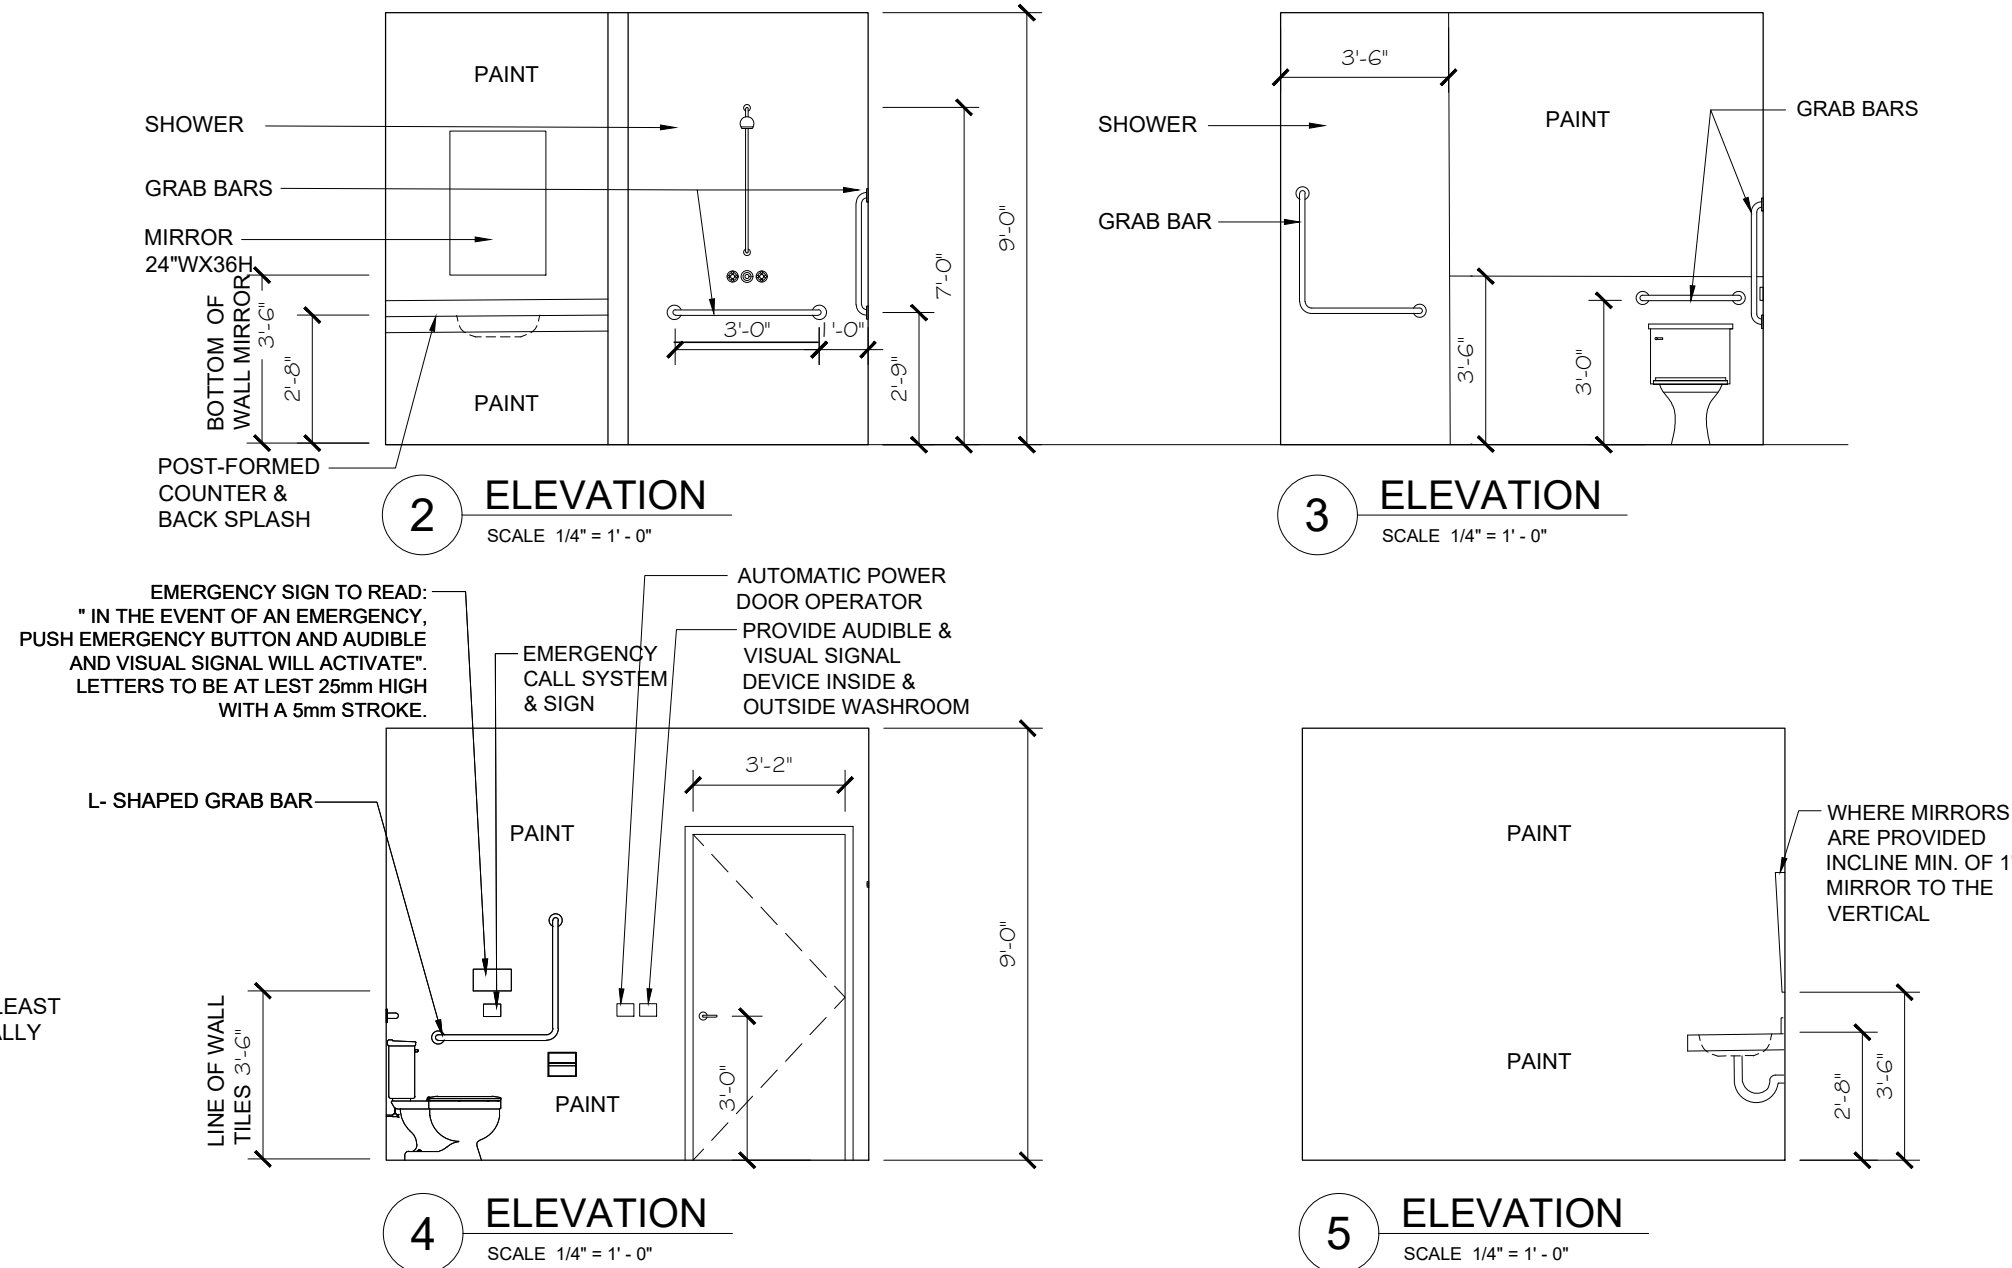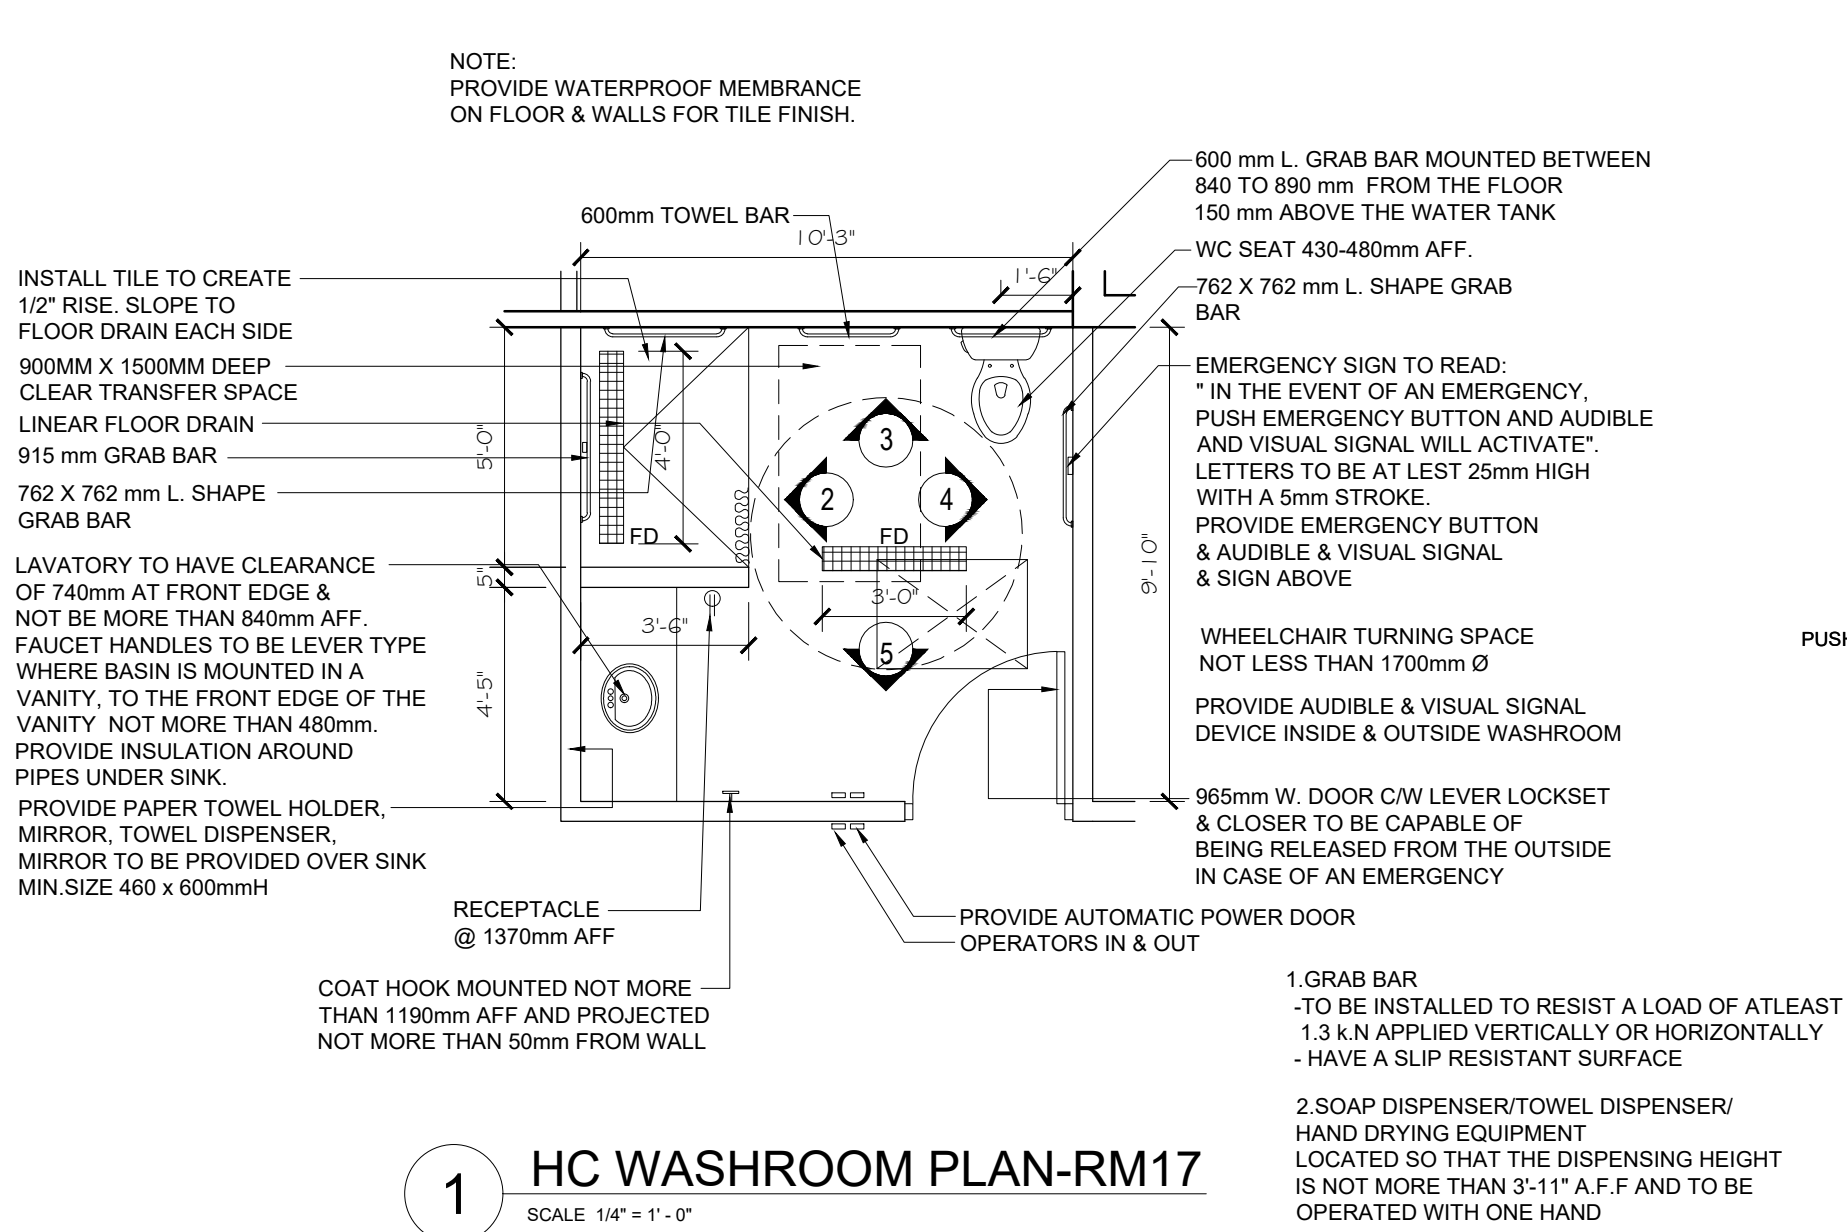

6 W446

7 SECTION BETWEEN EXISTING & NEW CONSTRUCTION
SCALE 3/4" = 1' - 0"

No. ISSUED FOR DATE

1 TENDER 2026-08-10

No. REVISION DATE

- DO NOT SCALE DRAWINGS
- ALL DIMENSIONS TO BE CHECKED
AND VERIFIED ON THE JOB
- ALL DRAWINGS AND SPECIFICATIONS
ARE THE PROPERTY OF THE ARCHITECT

Marilyn Ypes
Architect Inc.

238 Twin Sister Lakes Road
Marmora, Ontario
K0K 2M0
Tel 613-472-2308



PROJECT

KOC DORM BLDG.
KINARK OUTDOOR
CENTRE

LOCATION :

1766 QUEEN'S LINE ROAD
TOWNSHIP OF MINDEN
HILLS

DRAWING

HC WASHROOM - DETAILS

SCALE
AS SHOWN

DATE
JULY 2025

DRAWN
L C

CHECKED
M Y

PROJECT NO.
2021- 42

DRAWING NO.

8

NOTES:

1. WATER SERVICE NEEDS TO BE LEFT ON TO PROVIDE WATER TO OTHER AREAS OF THE CAMP
2. PROVIDE CONSTRUCTION FENCING ALL AROUND THE CONSTRUCTION SITE.
3. ALL DISTURBED SOIL IS TO BE SEEDED WITH GRASS SEED AFTER BUILDING CONSTRUCTION.
4. PROVIDE CONCRETE PADS UNDER EACH PROPANE TANK AND EMERGENCY GENERATOR. SIZES 10FEET LONG BY 4 FEET WIDE FOR EACH PROPANE TANK AND 5 FEET X 3 FEET FOR THE GENERATOR. PADS TO BE 6" THICK WITH 6" X 6" - 10" X 10".

AREA OF EXISTING BUILDING 942.44 SQ.FT./87.55M²
AREA OF ADDITION 2096.00 SQ.FT./194.72M²
3038.44 SQ.FT./282.27M²


THIS IS A PART 9 BUILDING

DASHED LINE INDICATE 2 M SETBACK FROM TOP OF BANK. PROVIDE LARGE ROCKS EVERY 1M TO PREVENT CARS WITHIN 2M SETBACK

HATCHED AREA INDICATE LANDSCAPE RESTORATION AS PER NATURAL HERITAGE EVALUATION :

- SILT CONTROL ARE TO BE PROPERLY INSTALLED ALONG THE TOE OF ROCK SLOPE AND MAINTAINED GOOD WORKING ORDER UNTIL THE END OF MAY OF THE YEAR FOLLOWING PLANTING. WHILE TRADITIONAL SILT FENCING THAT IT PROPERLY IN THIS ARE SILT SOXX, A BIODEGRADABLE TUBE FILLED WITH WOOD CHIPS THAT CAN BE QUITE EASILY STAKED INTO THE GROUND, AND WHICH REQUIRES NO ONGOING MAINTENANCE ONCE PROPERLY INSTALLED;
- A GRADE-AL OR EXCAVATOR BE USED TO CAREFULLY DEPOSIT AND SPREAD A SANDY TOPSOIL INTO VOIDS IN THE ROCK, AT AN APPLICATION RATE OF 15 CM (1 M3 FOR EVERY 6.7 M2 OF AREA, OR 36 M3 IN TOTAL). IT IS NOTED THAT THIS WILL LEAVE SOME EXPOSED ROCK, BUT WILL FILL A CONSIDERABLE MOUNT OF THE VOIDS;
- NATIVE SHRUBS/SMALL TREES WHICH ARE RESISTANT TO OPEN, DRY SLOPE CONDITIONS ARE TO BE PLANTED AT A MAXIMUM SPACING OF AVERAGE 1.75 M APART. TO ACHIEVE THAT DENSITY, A MINIMUM 100 SHRUBS/TREES ARE TO PLANTED. SPECIES USED SHOULD ALSO BE ONE WHICH SPREAD VEGETATIVELY, AND WHICH THEREFORE SUBSTANTIALLY INCREASE THE DENSITY OF VEGETATION OVER THE SHORT- TO INTERMEDIATE-TERM. SUBSTANTIALLY INCREASE THE DENSITY OF VEGETATION OVER THE SHORT-TO INTERMEDIATE-TERM. A MINIMUM OF THREE OF THE FOLLOWING SPECIES ARE TO BE USED, WITH NO INDIVIDUAL SPECIES MAKING UP MORE 40% OF THE PLANTINGS:
STAGHORN SUMAC RHUS TYPHINA (1 GALLON POTTED STOCK)
SMOOTH SUMAC RHUS GLABRA (1 GALLON POTTED STOCK)
SNOWBERRY SYPHORICARPUS ALBUS (1 GALLON POTTED STOCK)
SERVICEBERRY AMELANCHIER CANADENSIS (1 GALLON POTTED STOCK)
PIN CHERRY PRUNUS PENSYLVANICA (1 GALLON POTTED STOCK)
ONCE PLANTED, THE SLOPES ARE TO BE ALLOWED TO NATURALIZE, WITH IT BEING RECOGNIZED THAT SOME OF THE PLANTINGS ARE NOT APT TO TAKE; 70% SURVIVALS CONSIDERED A SATISFACTORY OUTCOME.

1 SITE PLAN
SCALE 1:200

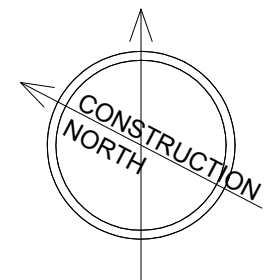

No.	ISSUED FOR	DATE
1	TENDER	2026-08-10

- DO NOT SCALE DRAWINGS
- ALL DIMENSIONS TO BE CHECKED AND VERIFIED ON THE JOB
- ALL DRAWINGS AND SPECIFICATIONS ARE THE PROPERTY OF THE ARCHITECT

Marilyn Ypes
Architect Inc.

238 Twin Sister Lakes Road
Marmora, Ontario
K0K 2M0
Tel 613-472-2308



PROJECT

KOC DORM BLDG.
KINARK OUTDOOR
CENTRE

LOCATION

1766 QUEEN'S LINE ROAD
TOWNSHIP OF MINDEN
HILLS

DRAWING

SITE PLAN

SCALE

1:200

DATE

JULY 2025

DRAWN

L C

CHECKED

M Y

PROJECT NO.

2021-42

DRAWING NO.

1