


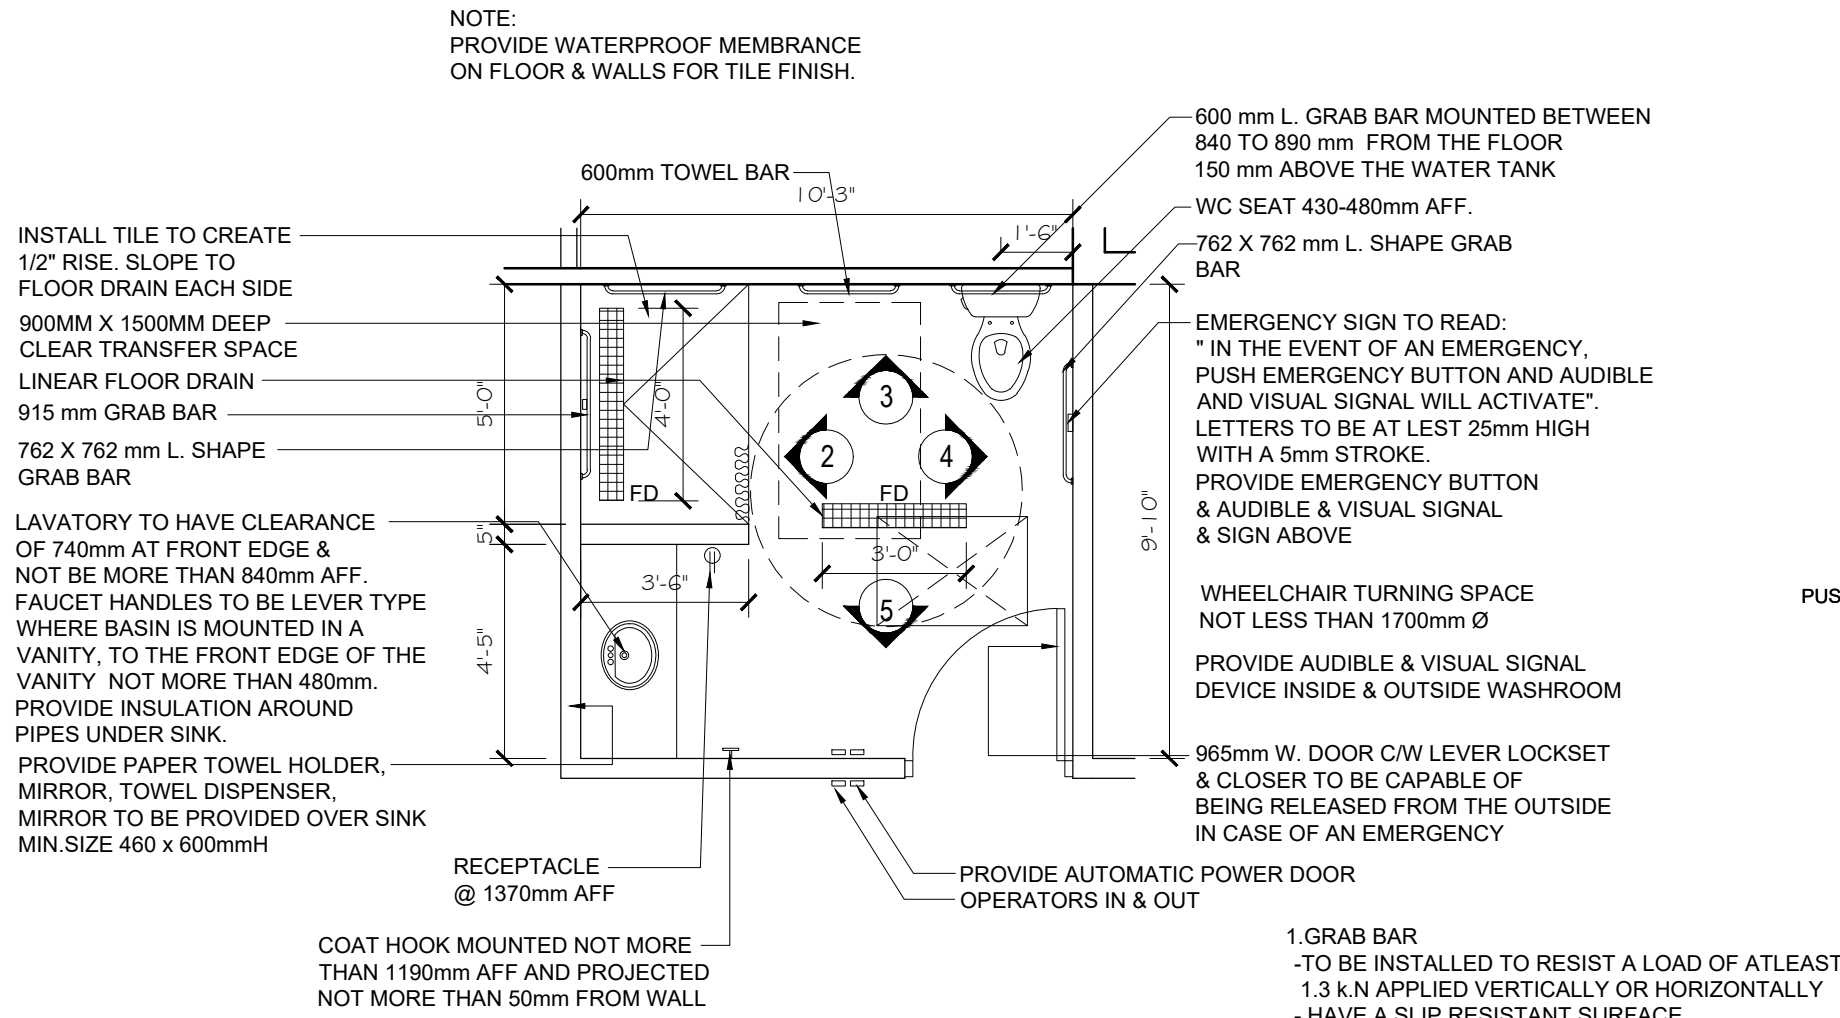


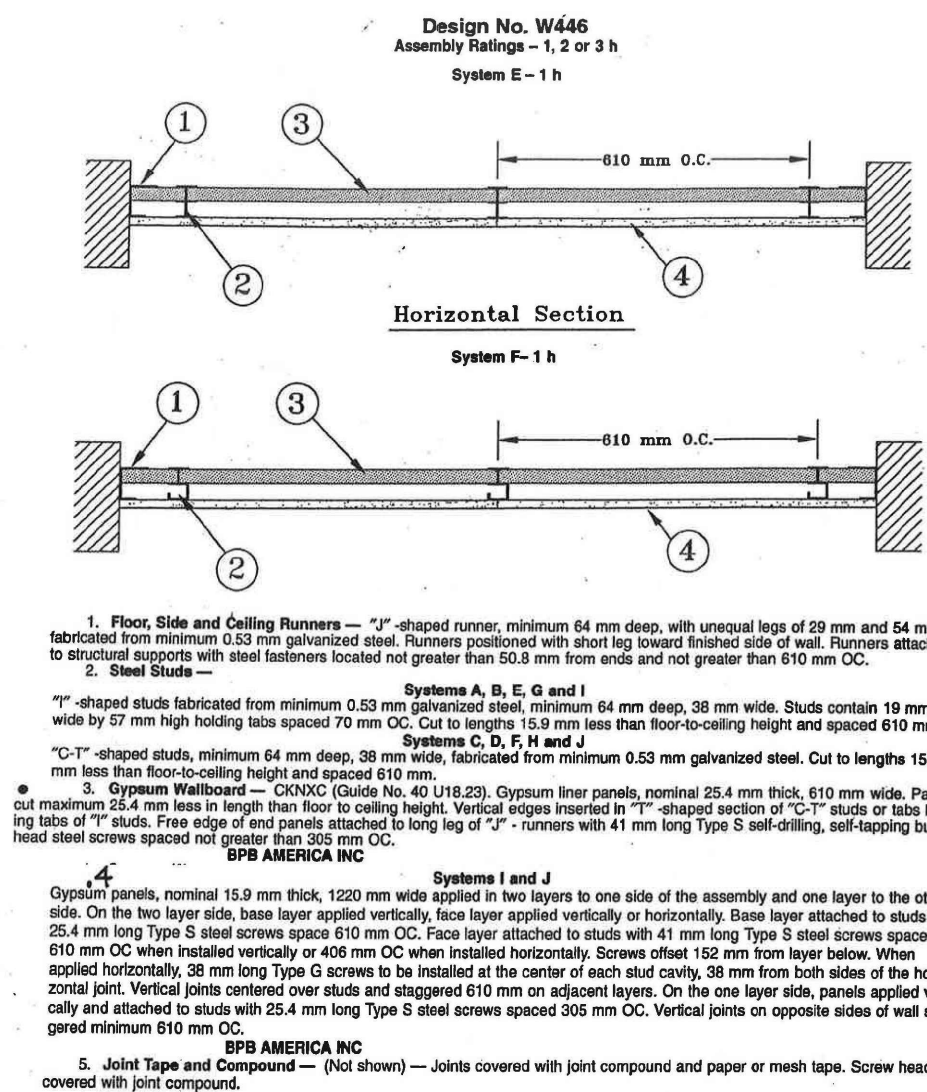

1 HC WASHROOM PLAN-RM17
SCALE 1/4" = 1' - 0"

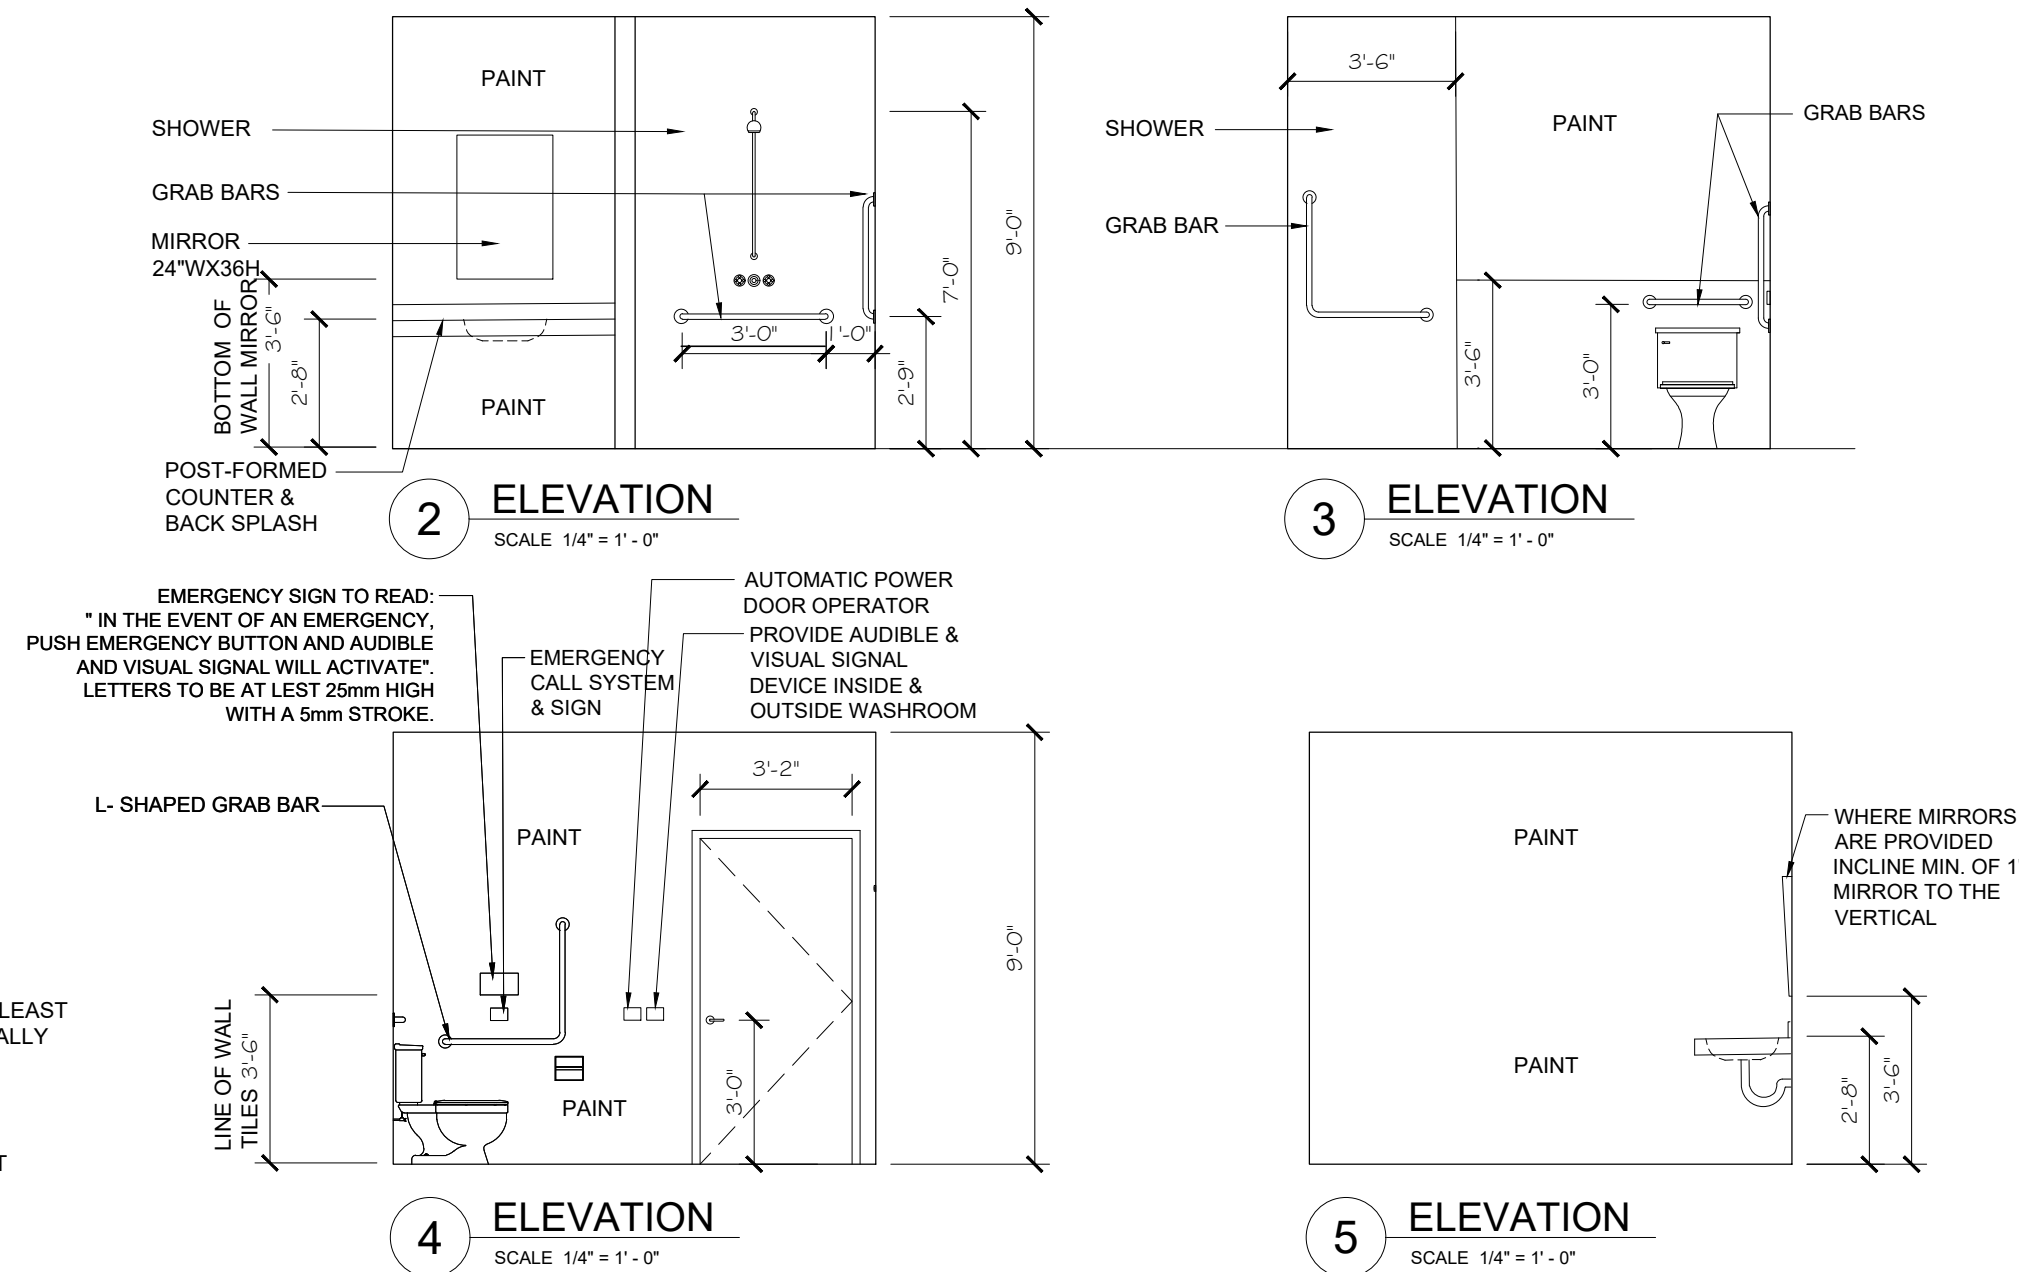

6 W446

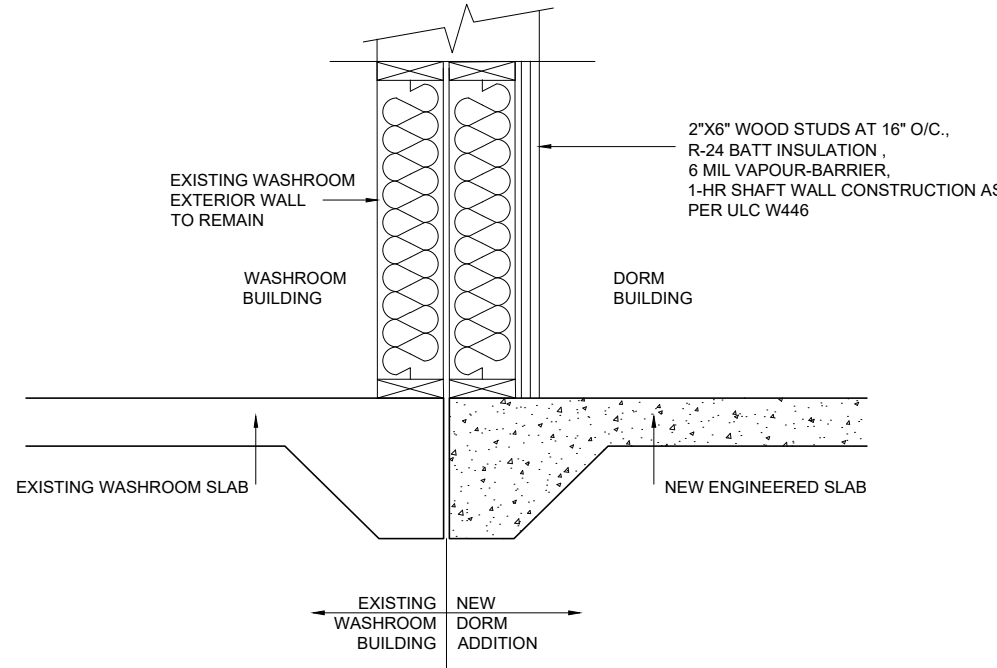

7 SECTION BETWEEN EXISTING & NEW CONSTRUCTION
SCALE 3/4" = 1' - 0"

No. ISSUED FOR DATE

1 TENDER 2026-08-10

No. REVISION DATE

- DO NOT SCALE DRAWINGS
- ALL DIMENSIONS TO BE CHECKED
AND VERIFIED ON THE JOB
- ALL DRAWINGS AND SPECIFICATIONS
ARE THE PROPERTY OF THE ARCHITECT

Marilyn Ypes
Architect Inc.

238 Twin Sister Lakes Road
Marmora, Ontario
K0K 2M0
Tel 613-472-2308



PROJECT

KOC DORM BLDG.
KINARK OUTDOOR
CENTRE

LOCATION :

1766 QUEEN'S LINE ROAD
TOWNSHIP OF MINDEN
HILLS

DRAWING

HC WASHROOM - DETAILS

SCALE
AS SHOWN

DATE
JULY 2025

DRAWN
L C

CHECKED
M Y

PROJECT NO.
2021- 42

DRAWING NO.
8